
SUPPLY SCOPE (distributor quantities, no material prices): Nudura ICF walls above the basement, pre-cut by BuildEase - LG 457 core (unassembled XR35 panels on insert webs + 4-way connectors, corners lapped straights, openings timber-bucked by others) and 8in Std internal walls on the transfer deck, GF / FF external walls in 6in XR35. The raft, existing basement, decks, slabs, steels, roof, windows, doors and partitions are shown in good faith only (design assumptions) - engineer / specialists to design.

QUOTATION - NOT FOR CONSTRUCTION

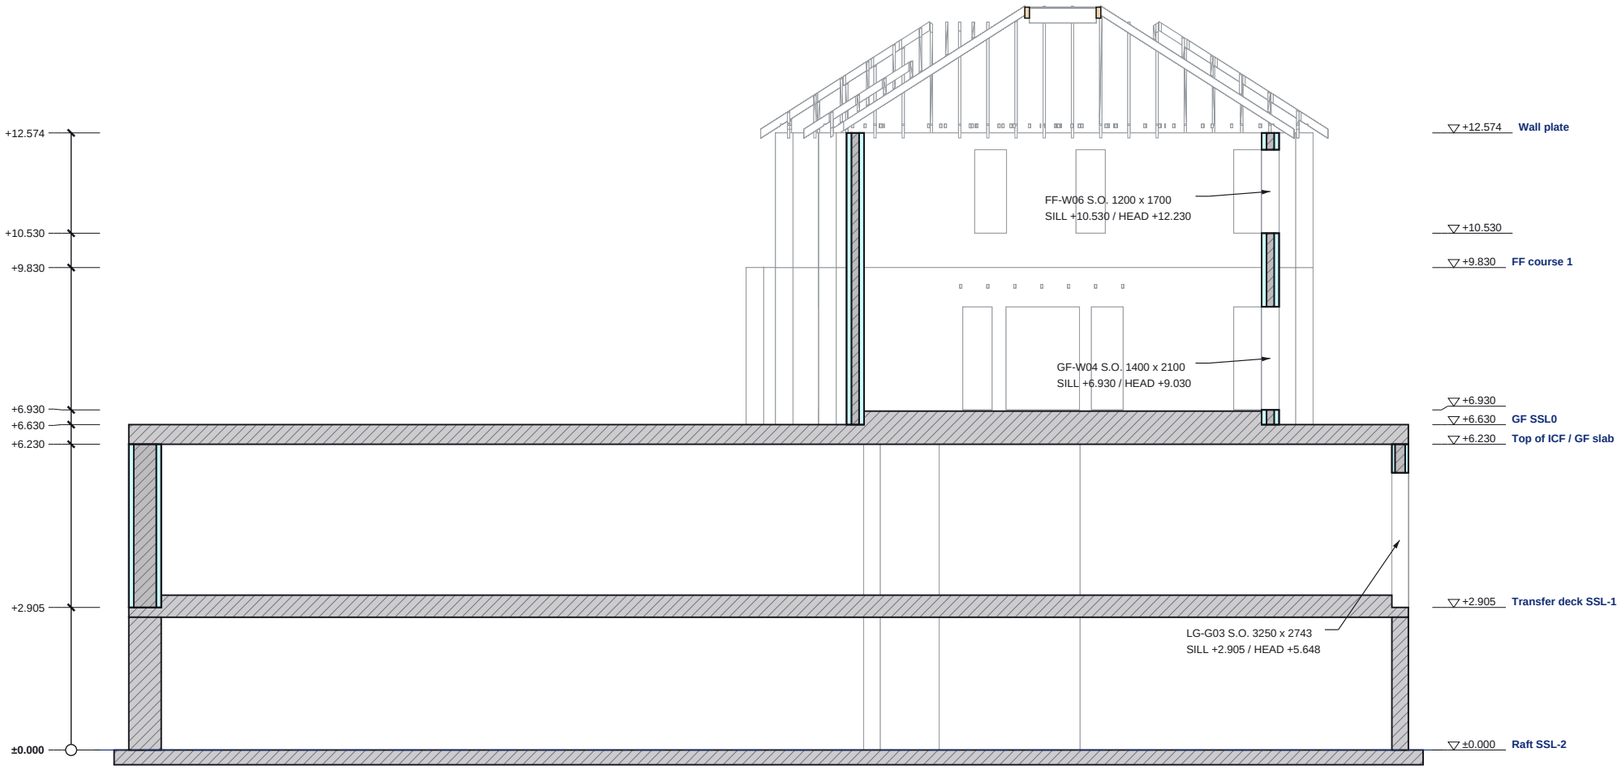

SECTION A-A

Scale 1:125 @ A3 | Looking west; levels above GF FFL

ICF EPS (cut)
ICF concrete core / RC (cut)
Steel (cut)
Timber (cut)
Beyond the cut (line work)


0 1 2 3 4 5m

SECTION A-A SCHEDULES

LEVELS ON THIS SECTION

Level	FFL
Raft SSL-2	±0.000
Transfer deck SSL-1	+2.905
Top of ICF / GF slab	+6.230
GF SSL0	+6.630
top of ICF W03	+6.930
FF course 1	+9.830
top of ICF W03	+10.530
Wall plate	+12.574

SECTION KEY

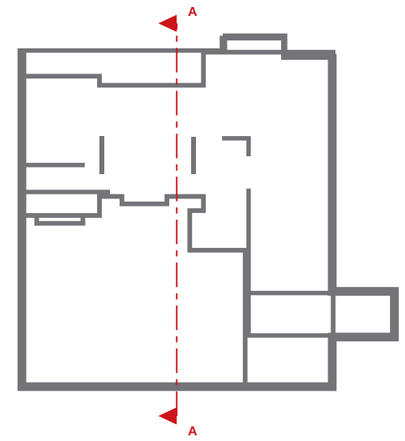

NOTES

1. Section A-A is a BuildEase ICF section (not an architect's section line). Cut elements hatched / filled; the model beyond the cut in line work.
2. Levels above GF FFL.
3. ICF: Nudura 6" XR35, 101.6 EPS + 152.4 core + 101.6 EPS = 355.6; 9.18in XR35 Panel Series, 101.6 EPS + 457.2 core + 101.6 EPS = 660.4; 8" Std, 66.7 EPS + 203.2 core + 66.7 EPS = 336.6, 457.2 core + 101.6 EPS = 660.4. BDI S1 02 shows 450 RC walls to the LG perimeter: modelled as a 457 core of unassembled Nudura XR35 panels on 12in + 6in insert webs (BDI to accept). GF / FF external walls converted to 6in XR35. Reinforcement, lintels, the FF deck ledger / bearing into the ICF and the indicative steels for the engineer.
4. Steel marks, BOS / TOS: BDI 20164022 rev C4. See ES26-088-GA-01 / EL-01 / EL-02 in the approval drawings pack.
5. Datum: 0 = raft SSL-2 (+40.357). Transfer deck SSL-1 +43.262, Top of ICF +46.587, GF SSL0 +46.987, FF SSL1 +50.297, U/S wall plate +52.962.
6. From BDI 20164022 S1 02 / S3 02 (C4), the architect's GF / FF plans and Ethos' extension sketch.

REVISIONS

REV	DATE	DESCRIPTION
-	02.11.26	Quotation issue

Nudura™ BuildEase

CLIENT	PROJECT
Ethos Property Developments (Nudura distributor) - Mark Whalley	House - walls above the basement, Badgers Hollow, Alderley Edge

DRAWING TITLE

SECTION A-A

ICF section with levels and build-ups

SCALE	SIZE	DATE
1:125	A3	02.11.26
DRAWN: TS	CHECKED	APPROVED

STATUS	DRAWING No.	REV
QUOTATION	ES26-088-SE-01	-

Do not scale. All dimensions in millimetres; levels in metres from GF FFL. Check all dimensions on site.